


AGUJAS	P.K.
75	107/367

SEÑALES	P.K.
E2	107/653

AGUJAS	P.K.
2	107/653
4	108/060
6	108/110
3	108/374
1	108/454

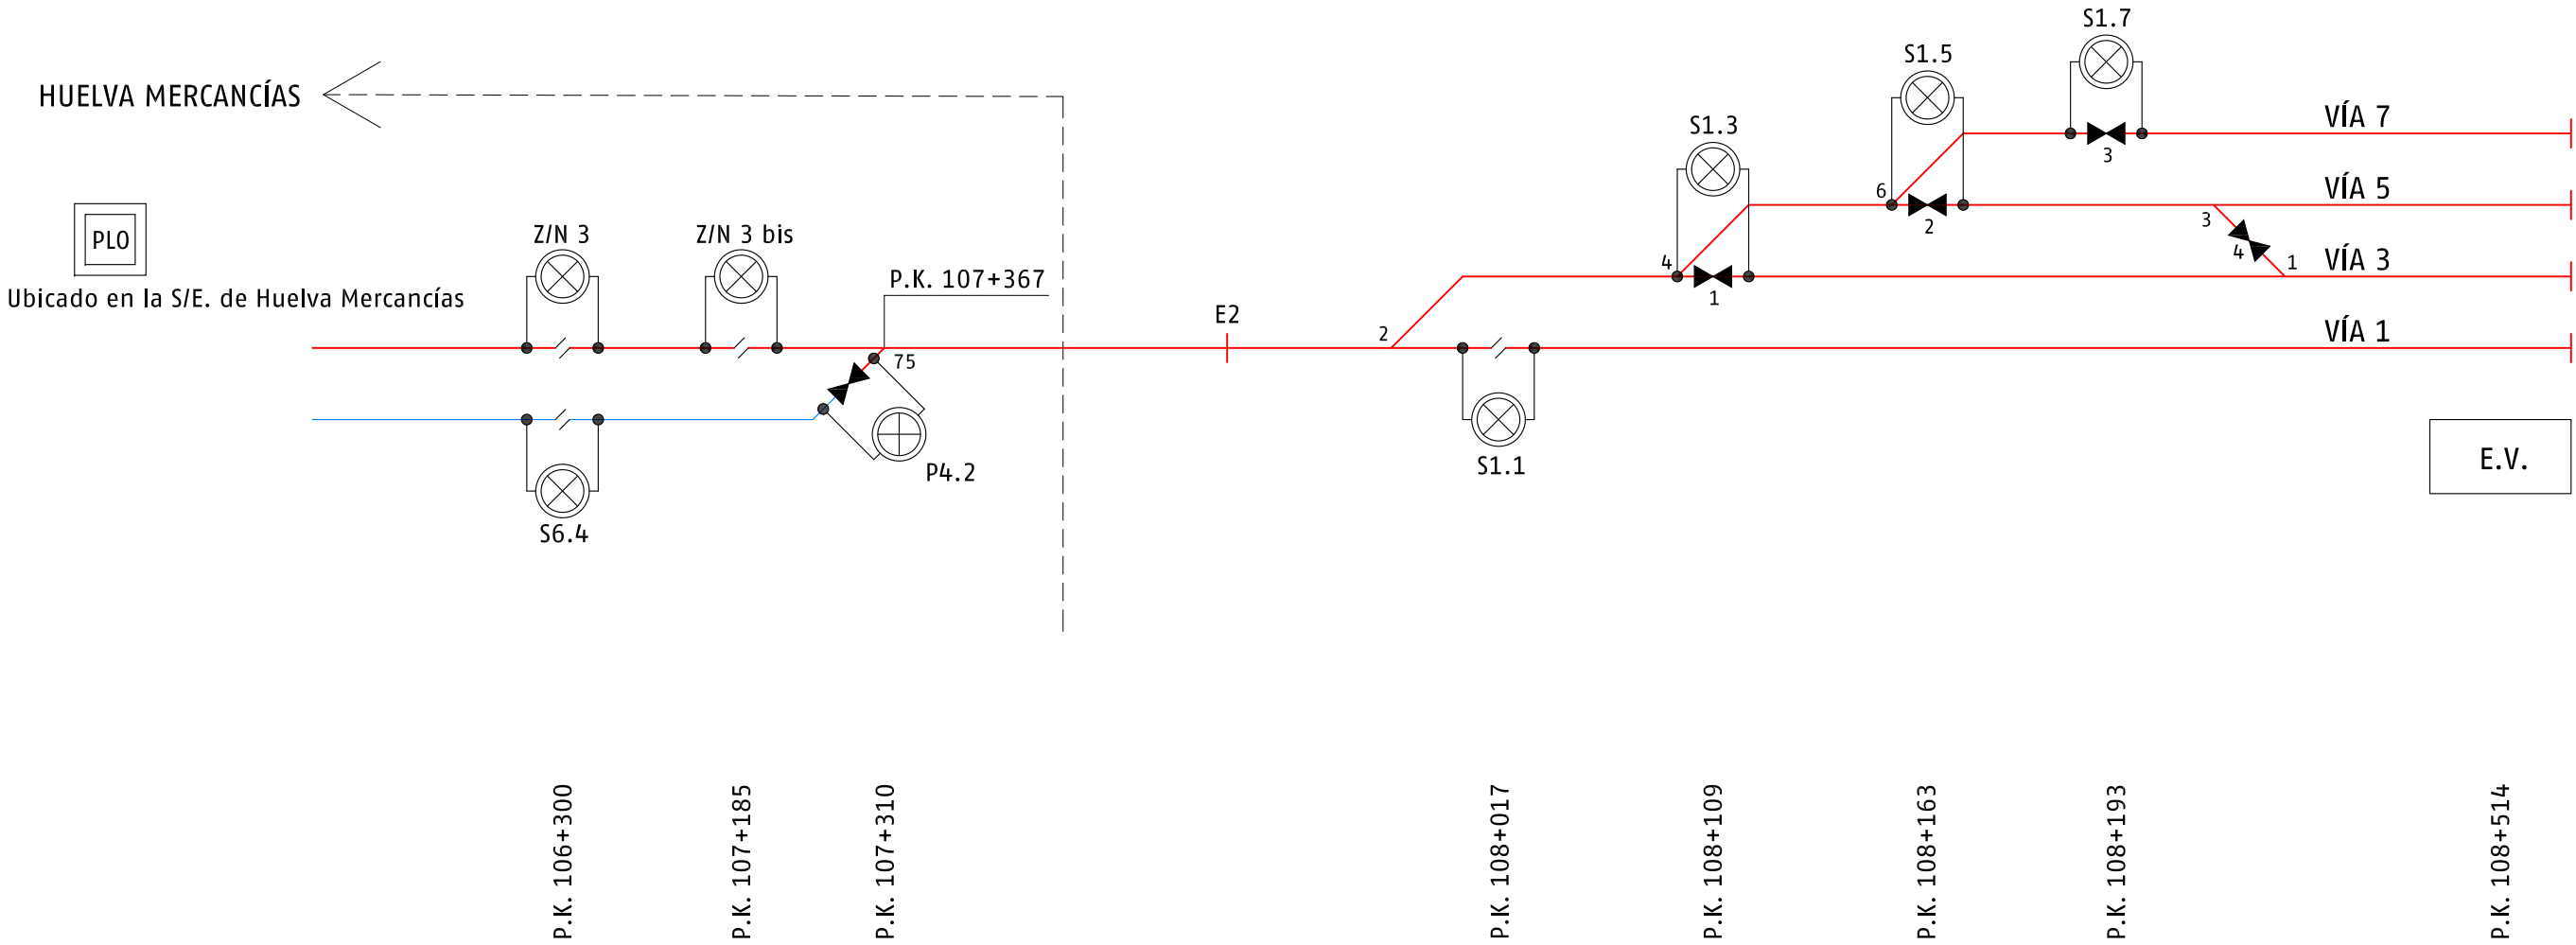

SUBDIRECCIÓN DE OPERACIONES
RED CONVENCIONAL SUR
JEFATURA DE ÁREA DE
MANTENIMIENTO DE SEVILLA

Dibujado por: J.G.J.
Aprobado por: Jose Angel Gomez Flores
Firma:
Fecha: 19-JULIO-2024

ESQUEMA ELÉCTRICO L.A.C.
P.E. 26 LÍNEA DE BIF. LOS NARANJOS A HUELVA
HUELVA

Plano nº 3-S-H
Sustituye a:
Hoja nº 17 de 17